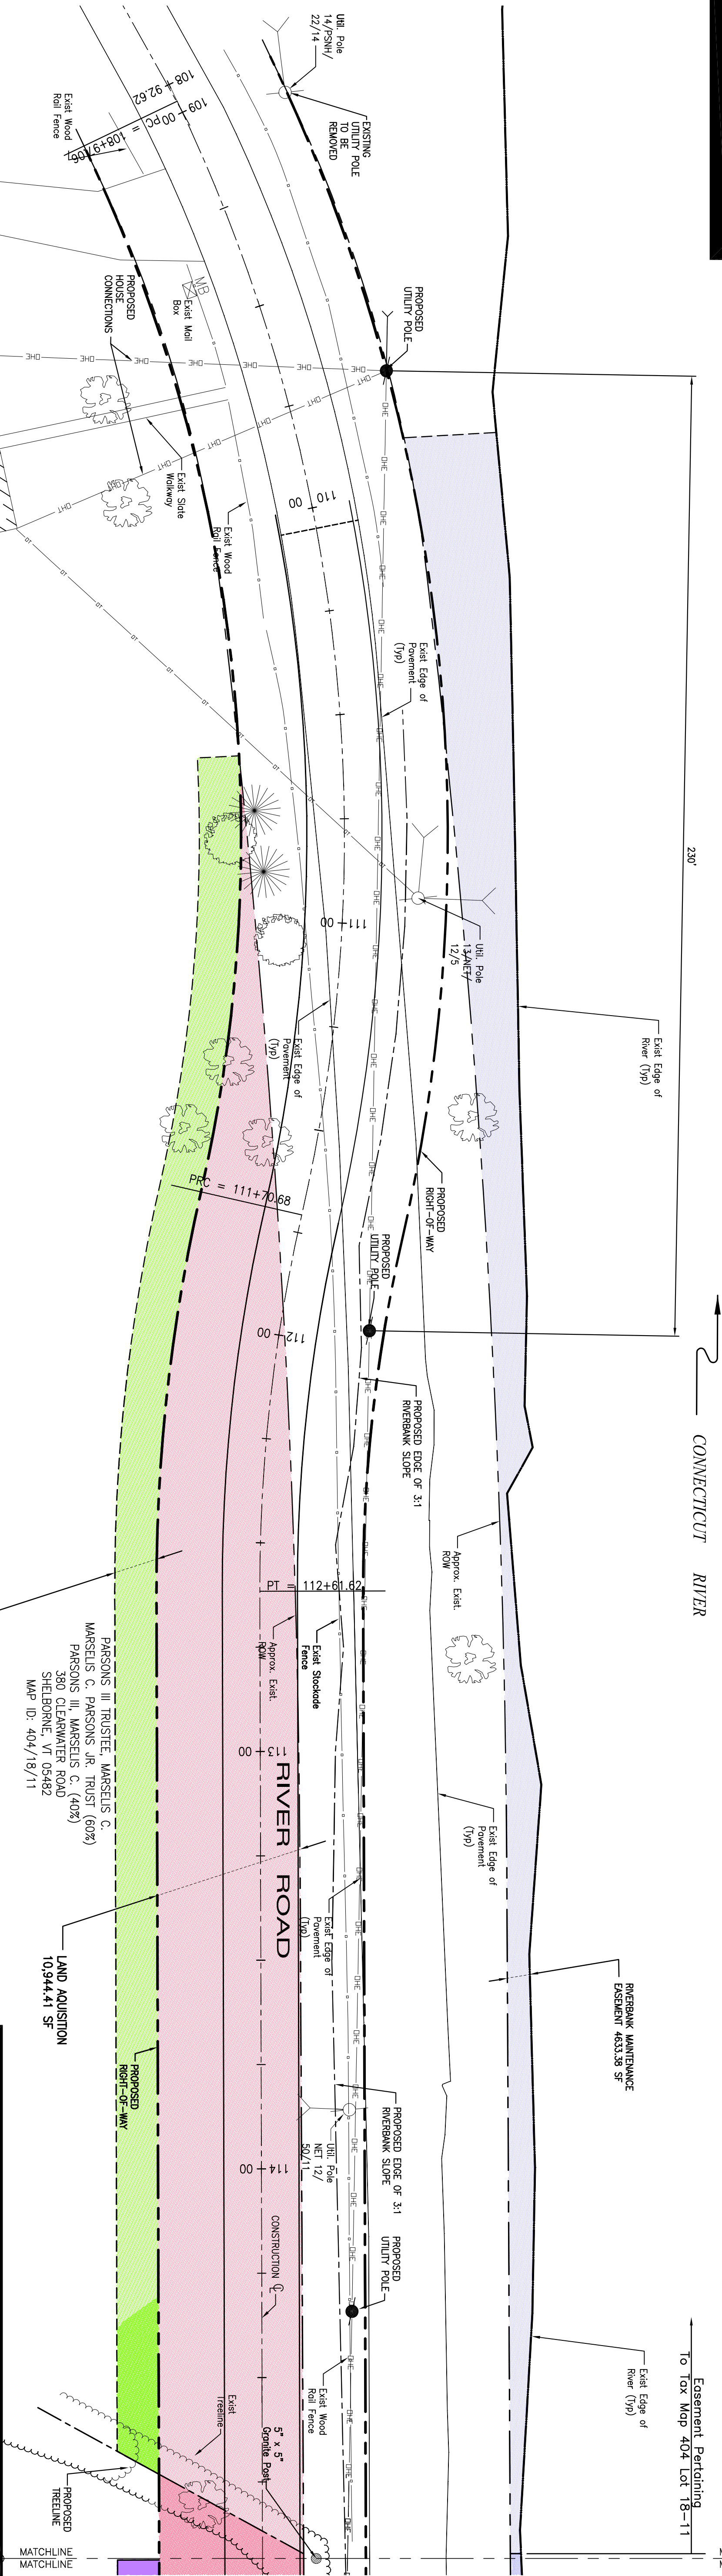
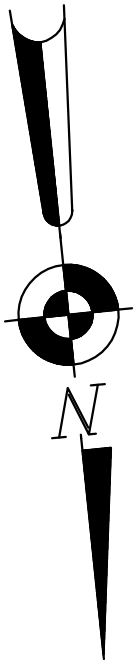


[illegible]

Lyme, Grafton County, New Hampshire
11-09-11

LAND ACQUISITION PLAN
Boundary Survey
MARSELIS C. PARSONS JR., MARSELIS C. PARSONS I
& CAROLA B LEA TRUST
Map 404, Lot 18-11 & 16-11

Scale: 1"=20'

Dr. By: VM Ck By: L

H.T.E. Job No. 1170001

Field Book No. 1177

Field Book Page No. 0

Sheet No. 1 of 2



A horizontal graphic scale bar with alternating black and white segments. It is marked with the numbers 0, 20, and 40. Below the bar, the text "SCALE IN FEET" is printed.

HOLDEN

ENGINEERING
SURVEYING, inc.

☐ 56 Old Succock Road - Unit #4
PO Box 480 Concord, N.H. 03302
(603) 225-6449

☐ 9 Constitution Drive
Bedford, N.H. 03110
(603) 412-2078

All Rights Reserved.
No part of this plan may be reproduced or utilized
without the express permission of Holden Engineering & Surveying.